

# ESCOLA TRANSITÓRIA MODELO RURAL

João Figueredo Lima, Lelé

## O ARQUITETO

João Filgueiras Lima, mais conhecido como Lelé, foi um dos mais importantes arquitetos brasileiros do século XX. Nascido no Rio de Janeiro em 1931, Lelé formou-se pela Faculdade Nacional de Arquitetura da Universidade do Brasil e ficou conhecido por sua forte atuação em projetos públicos, especialmente nas áreas da saúde, educação e urbanismo. Trabalhou em estreita colaboração com nomes como Oscar Niemeyer e Darcy Ribeiro, sendo um dos principais responsáveis pela concepção e desenvolvimento dos Centros Integrados de Educação Pública (CIEPs) no Rio de Janeiro e da Rede Sarah de Hospitais de Reabilitação.

Lelé destacou-se por sua abordagem inovadora, voltada para a industrialização da construção civil e a racionalização dos processos construtivos. Seu trabalho é marcado pela busca de soluções funcionais, econômicas e sustentáveis, sem abrir mão da qualidade arquitetônica e do compromisso social. Foi também um dos pioneiros no uso de pré-moldados de concreto e estruturas metálicas leves, sempre pensando em sistemas construtivos eficientes e replicáveis. Sua arquitetura humanista e voltada ao bem-estar coletivo deixou um legado expressivo na paisagem urbana brasileira e na história da arquitetura moderna.


Lelé também se destacou por sua atuação na área da saúde, especialmente com os hospitais da Rede Sarah. Nesses projetos, uniu eficiência técnica, conforto ambiental e soluções construtivas inovadoras. Sua arquitetura buscava sempre atender às necessidades humanas, com foco na funcionalidade e no bem-estar dos usuários.

## ESCOLA EM ABADIÂNIA


A Escola Transitória Modelo Rural, idealizada por João Filgueiras Lima (Lelé), foi desenvolvida na década de 1980 para atender comunidades rurais com infraestrutura educacional rápida e eficiente. O projeto utilizava sistemas construtivos industrializados, com módulos pré-fabricados que permitiam montagem ágil, baixo custo e fácil adaptação ao clima e ao terreno. Além da funcionalidade, a proposta prezava pelo conforto ambiental, com soluções de ventilação natural e sombreamento. A escola é um exemplo claro da busca de Lelé por uma arquitetura comprometida com a inclusão social e o acesso igualitário à educação.

Além de sua eficiência construtiva, a Escola Transitória Modelo Rural refletia uma preocupação com a dignidade dos usuários. Mesmo sendo pensada como solução provisória, ela oferecia espaços bem iluminados, ventilados e adaptados às condições locais, garantindo um ambiente adequado para o aprendizado. Esse cuidado revela a visão de Lelé sobre a arquitetura como instrumento de transformação social, capaz de melhorar a qualidade de vida mesmo em contextos com recursos limitados.

## O PROJETO

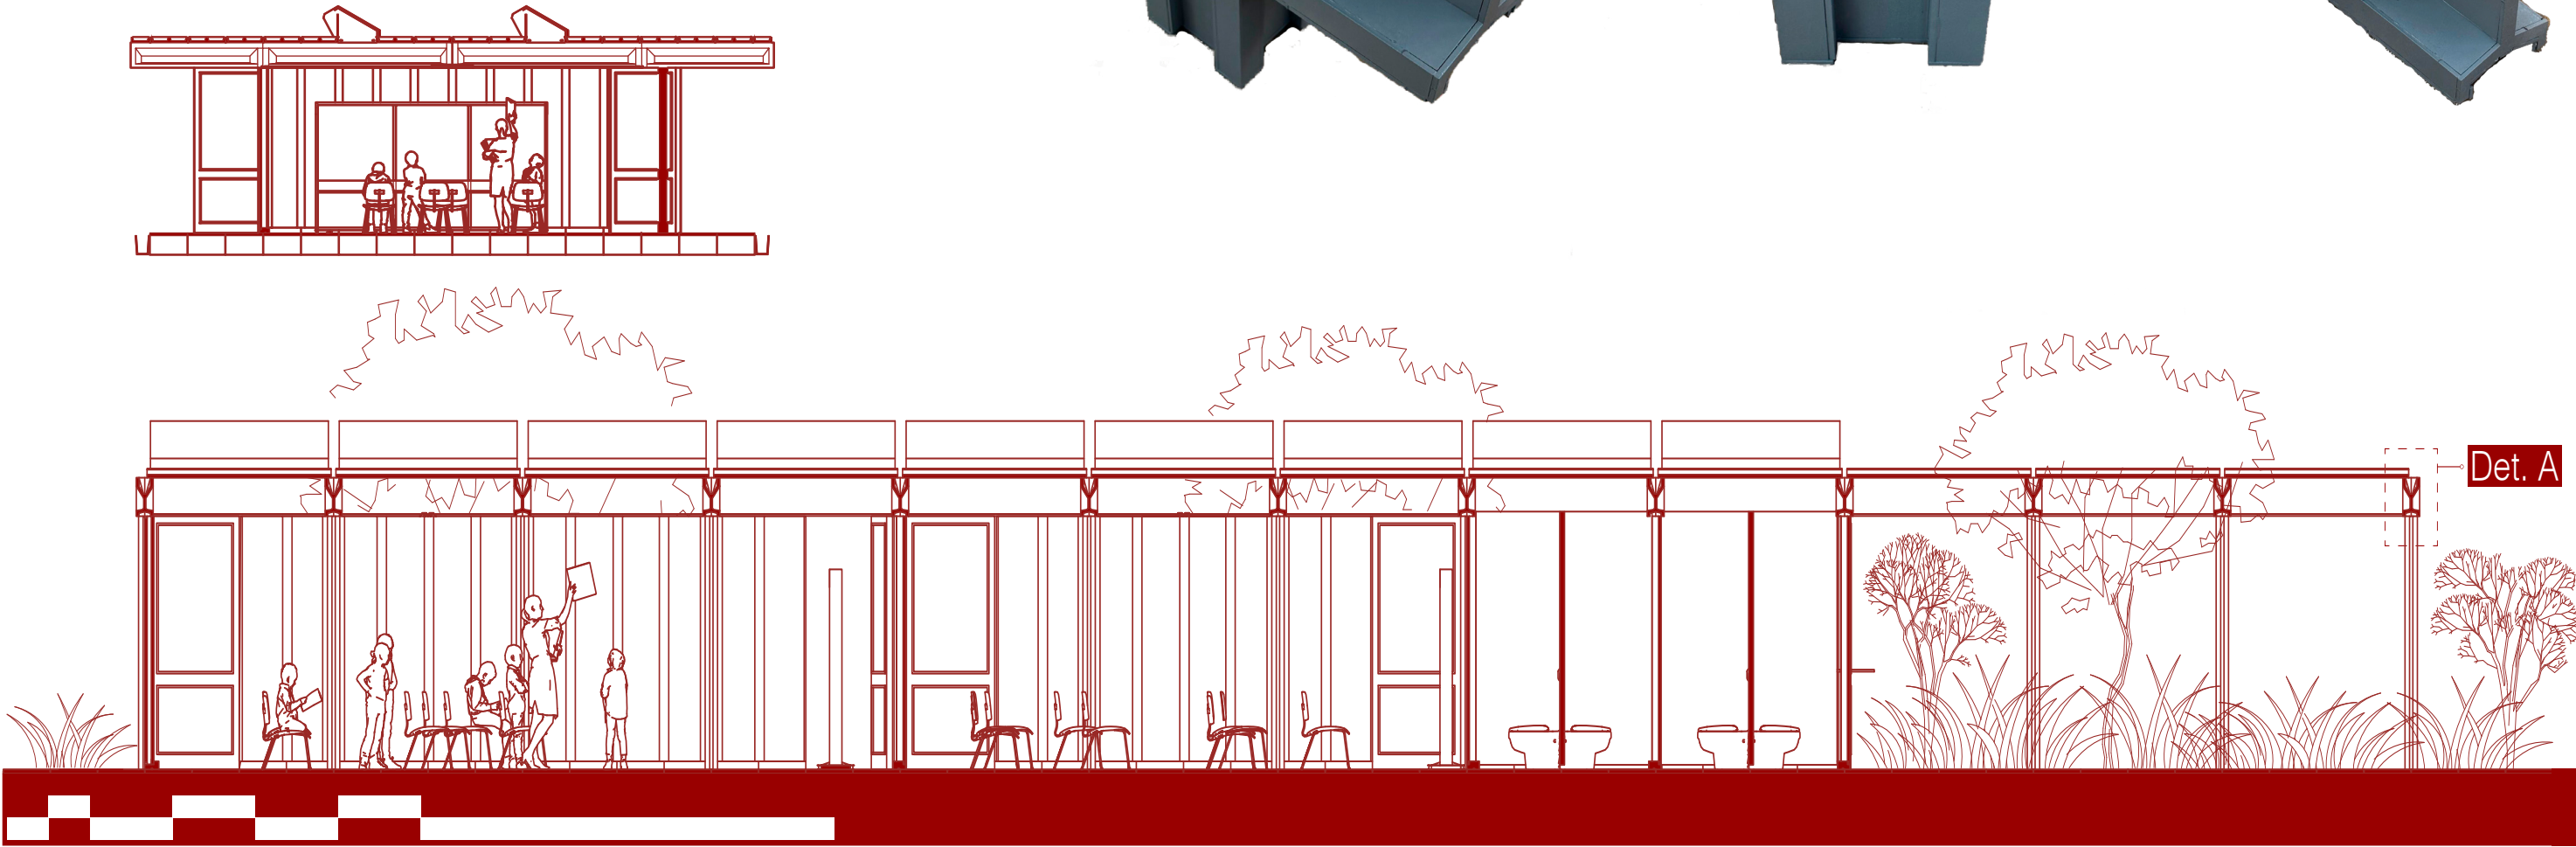

## PERSPECTIVA EXPLODIDA

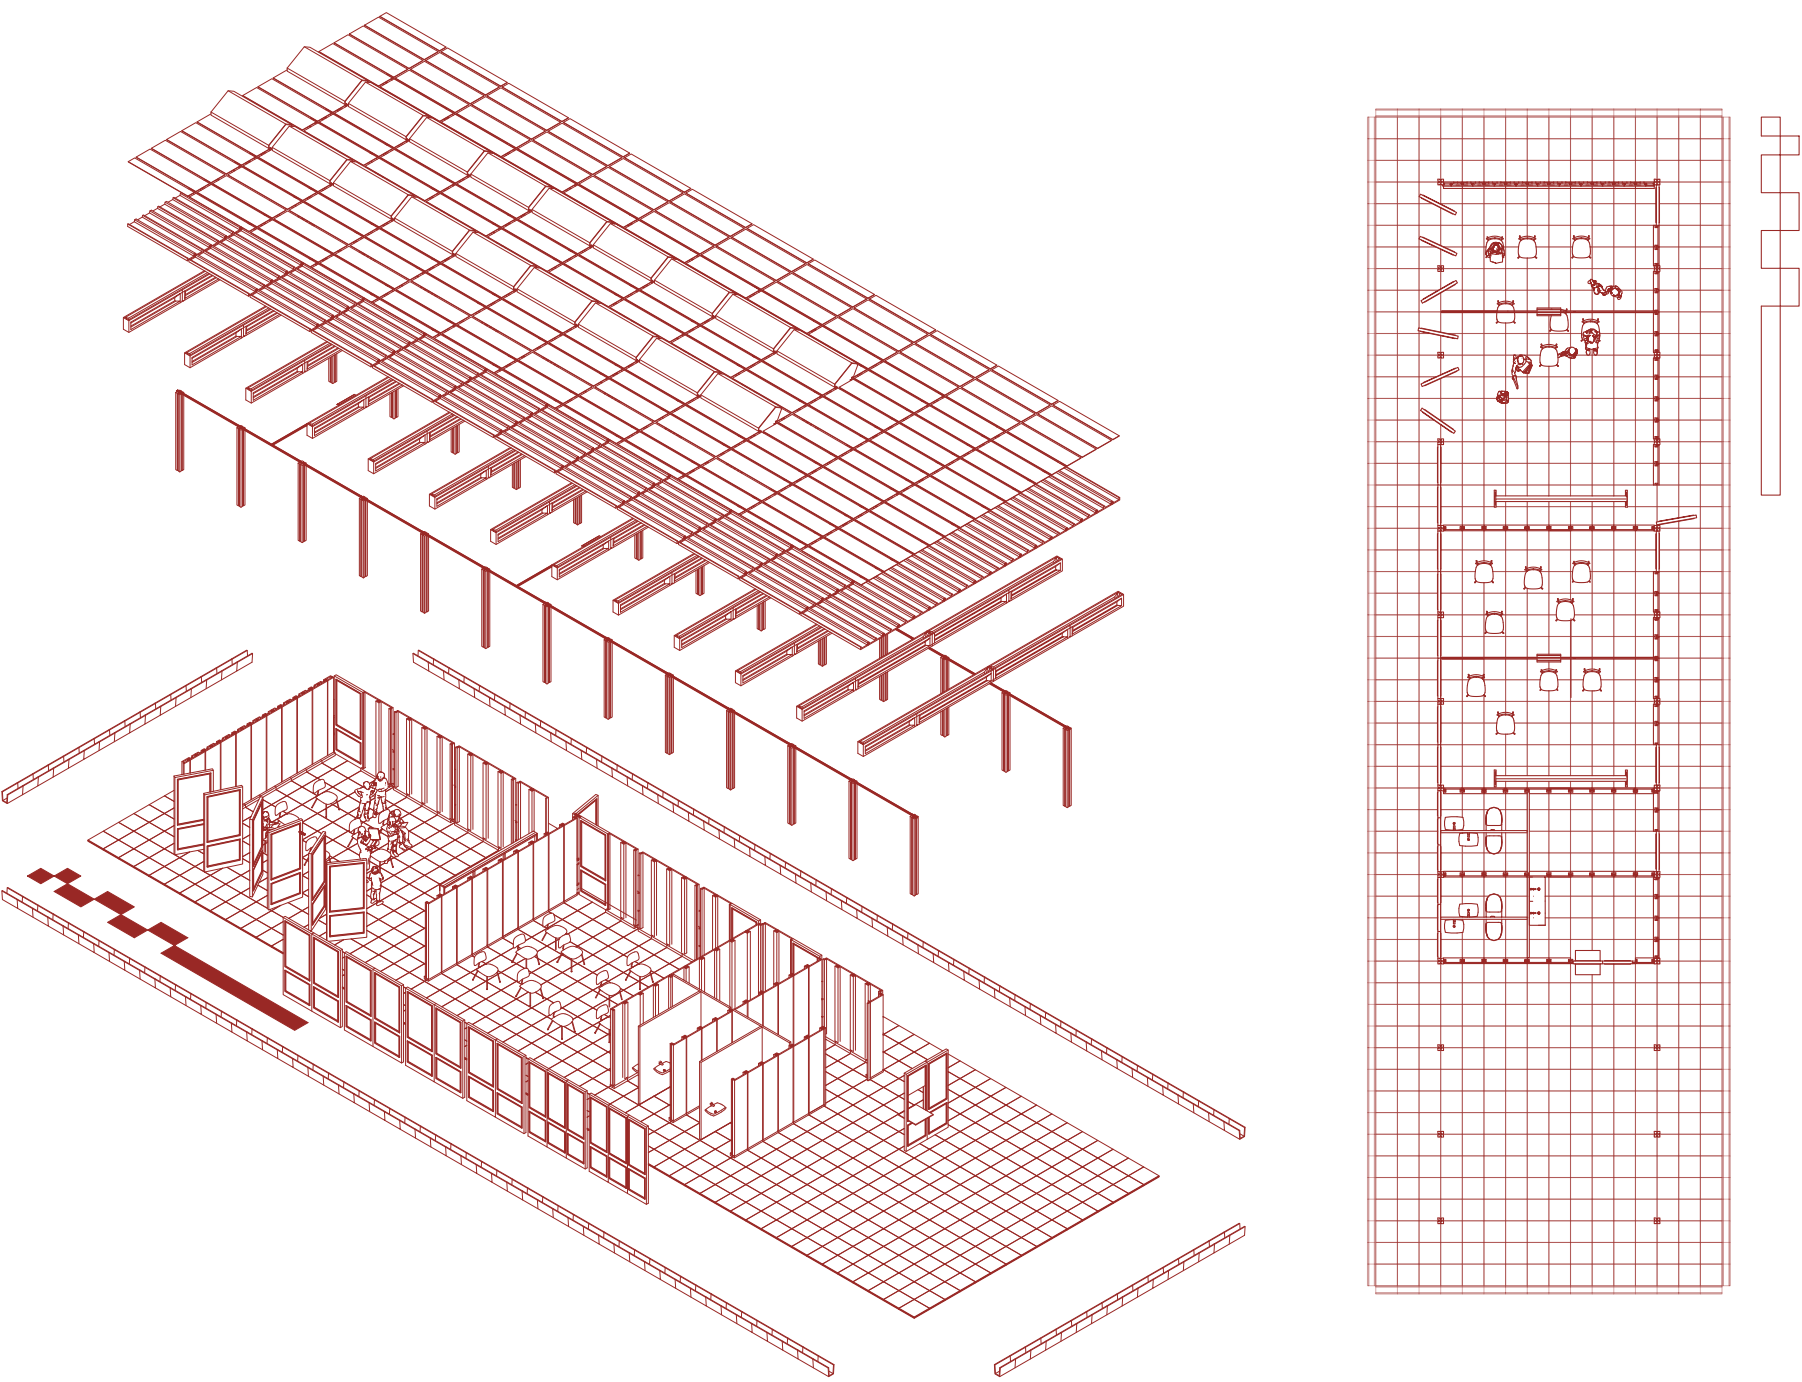

## DETALHE CONSTRUTIVO

